


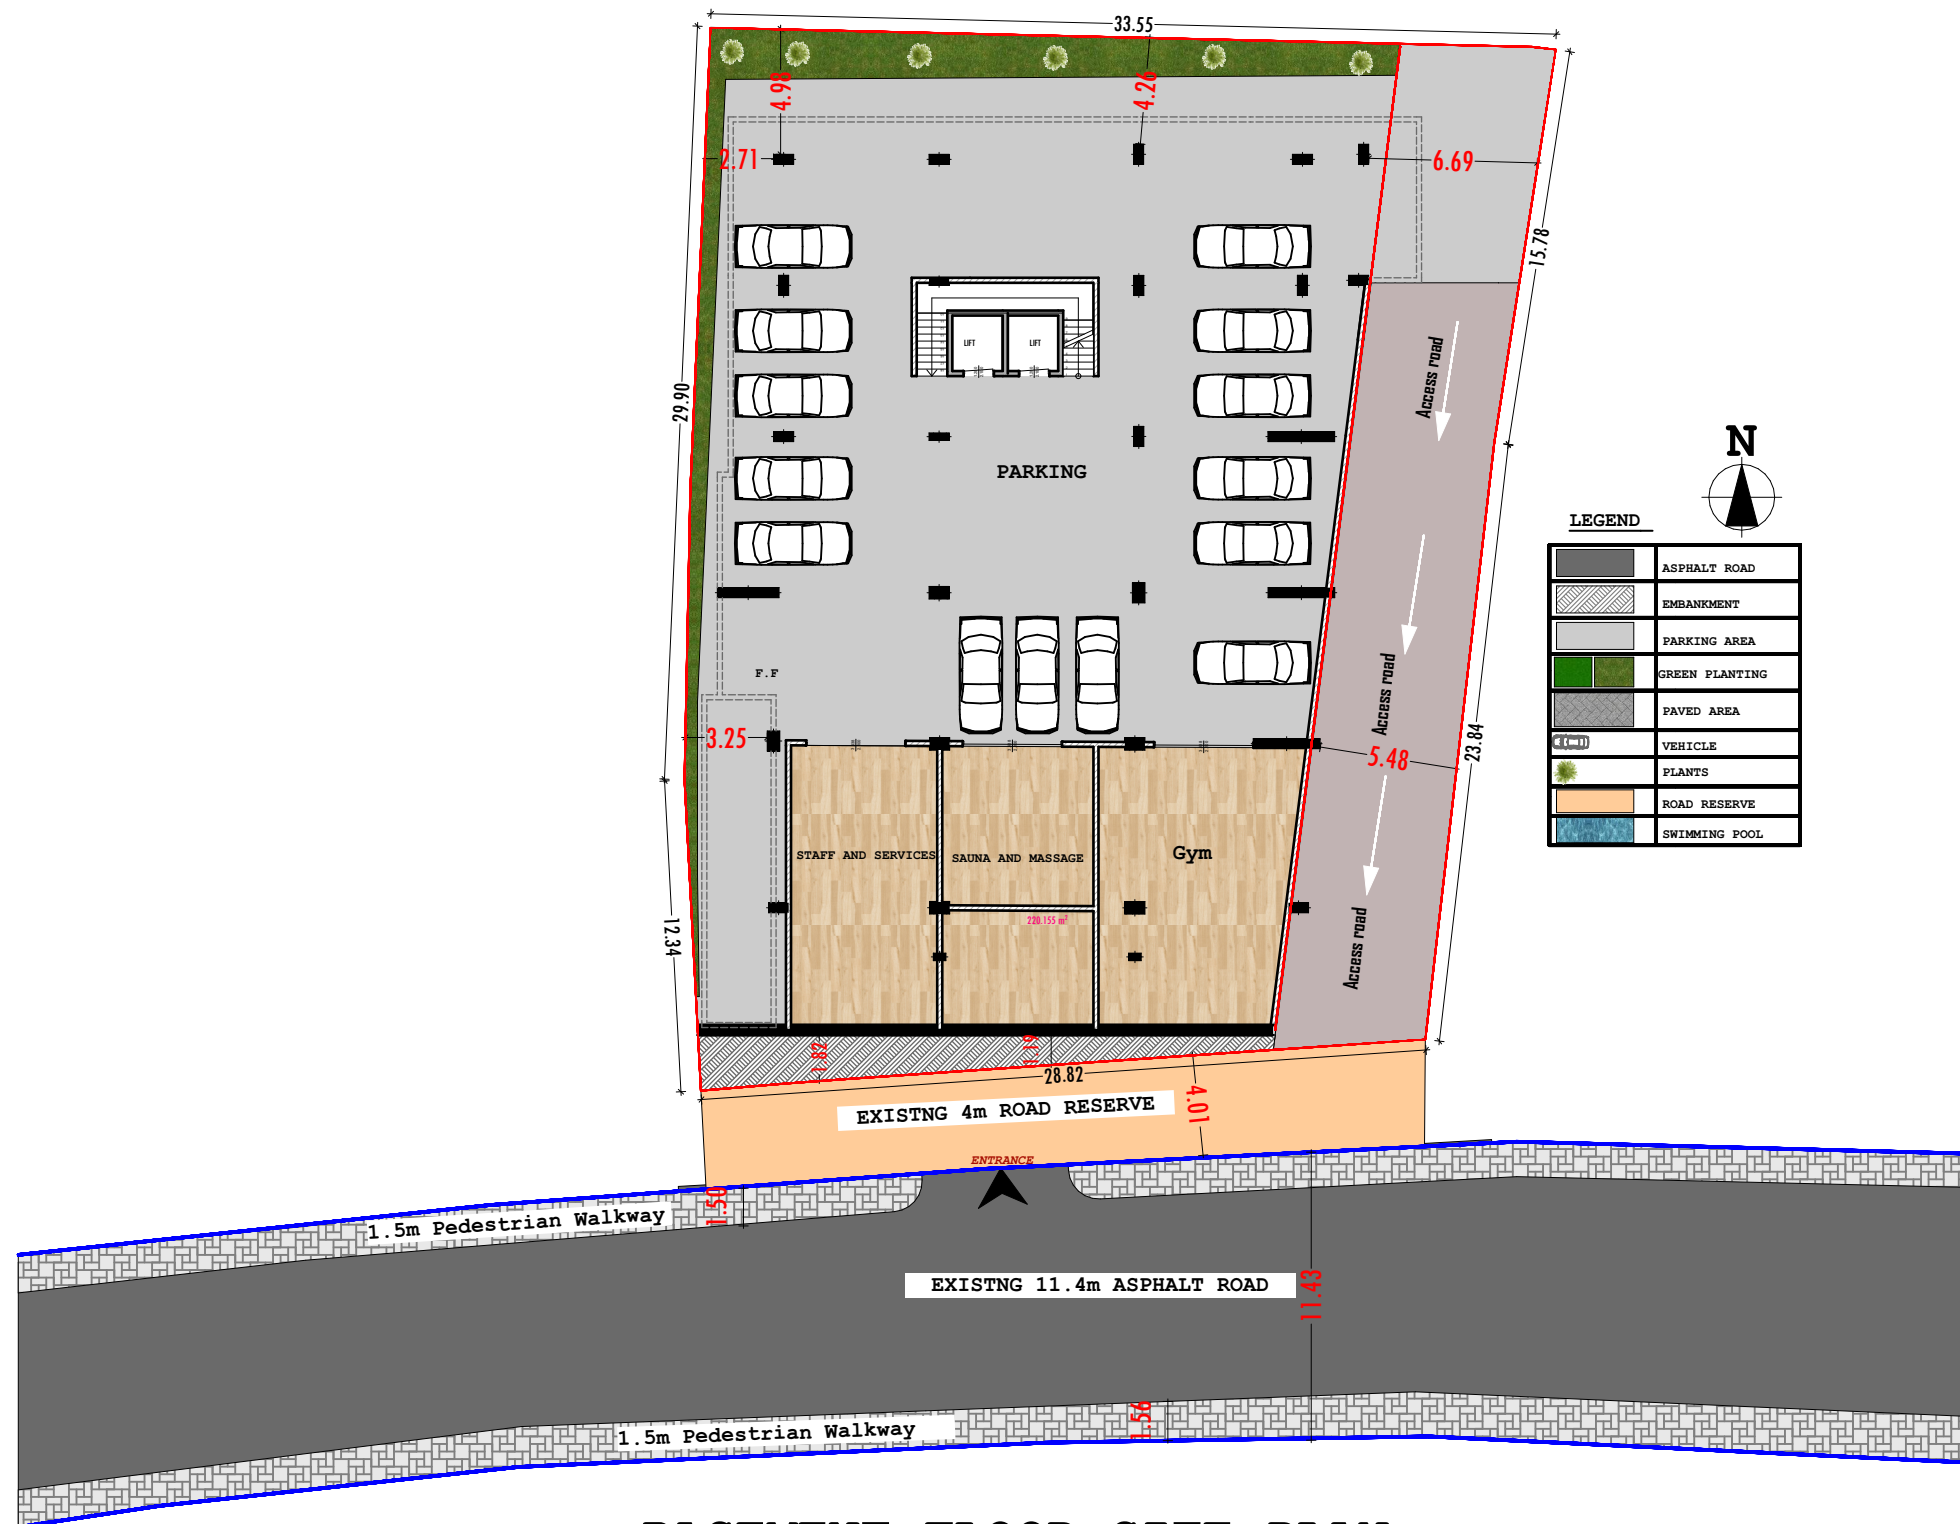

BASEMENT FLOOR SITE PLAN

REPUBLIC OF RWANDA
KIGALI CITY
GASABO DISTRICT
KIMIHURURA SECTOR
KIMIHURURA CELL
AMAJYAMBERE VILLAGE

NOTES
All dimensions to be checked on site for all discrepancies and confirm with the architect.
DPC course to be provided under all walls.
Drainage under driveways and slabs to be encased in 150mm thick concrete surround.
All plumbing and drainage works to comply with M.O.H regulations.
All basins, bath, and sink to be fitted with anti vacuum taps.
All softwood to be cured and approved to be polished and painted.
All S&WV to be approved 100mm dia p.v.c. pipe encased with chicken mesh and concrete surround to be plastered and painted or finished in ceramic tiles.
Plinth level to be a minimum 500mm from proposed parking level or existing ground level.

RAINWATER
all pitched roofs to have 100*150mm 22 gauges, box gutter and 75mm dia p.v.c down pipes in duct and other appropriate accessories all to be painted.
mortar for bonding to be strictly 1:4 mixing ratio

COPYRIGHT
This drawing is protected under the copyright act, and cannot be used or reproduced in part or in whole without the architect's approval

LEAD CONSULTANTS
RAFIKI
CONSTRUCTION COMPANY
B.P 3690, Tel: +250 - 788328442, Cell: +250 - 782566222
KIGALI - RWANDA

Owner:
NATAN PRIME LTD
PLOT N0: 1/02/08/02/1094 Kimihurura

DATE
Wednesday, 23 September 2026
Drawn by:
RCC Ltd
Checked by:
RCC Ltd
Zone: C1
Area: 1,276sqm
SCALE:
1:300

DOCUMENTS
BASEMENT FLOOR
SITE PLAN



REPUBLIC OF RWANDA
KIGALI CITY
GASABO DISTRICT
KIMIHURURA SECTOR
KIMIHURURA CELL
AMAJYAMBERE VILLAGE

NOTES
All dimensions to be checked on site for all discrepancies and confirm with the architect.
DPC course to be provided under all walls.
Drainage under driveways and slabs to be encased in 150mm thick concrete surround.
All plumbing and drainage works to comply with M.O.H regulations.
All basins, bath, and sink to be fitted with anti vacuum taps.
All softwood to be cured and approved to be polished and painted.
All S.W.V.P to be approved 100mm dia p.v.c. pipe encased with chicken mesh and concrete surround to be plastered and painted or finished in ceramic tiles.
Plinth level to be a minimum 500mm from proposed parking level or existing ground level.

RAINWATER
all pitched roofs to have 100*150mm 22 gauges box gutter and 75mm dia p.v.c down pipes in duct and other appropriate accessories all to be painted.
mortar for bonding to be strictly 1:4 mixing ratio


COPYRIGHT
This drawing is protected under the copyright act, and cannot be used or reproduced in part or in whole without the architect's approval

LEAD CONSULTANTS
RAFIKI
CONSTRUCTION COMPANY
B.P 5690, Tel: +250 - 788339442, Cell: +250 - 782566222
KIGALI - RWANDA

Owner:
NATAN PRIME LTD
PLOT N0: 1/02/08/02/1094 Kimihurura

DATE
Wednesday, 23 September 2026
Drawn by:
RCC Ltd
Checked by:
RCC Ltd
Zone: C1
Area: 1,276sqm
SCALE:
1:280

DOCUMENTS
GROUND FLOOR
SITE PLAN

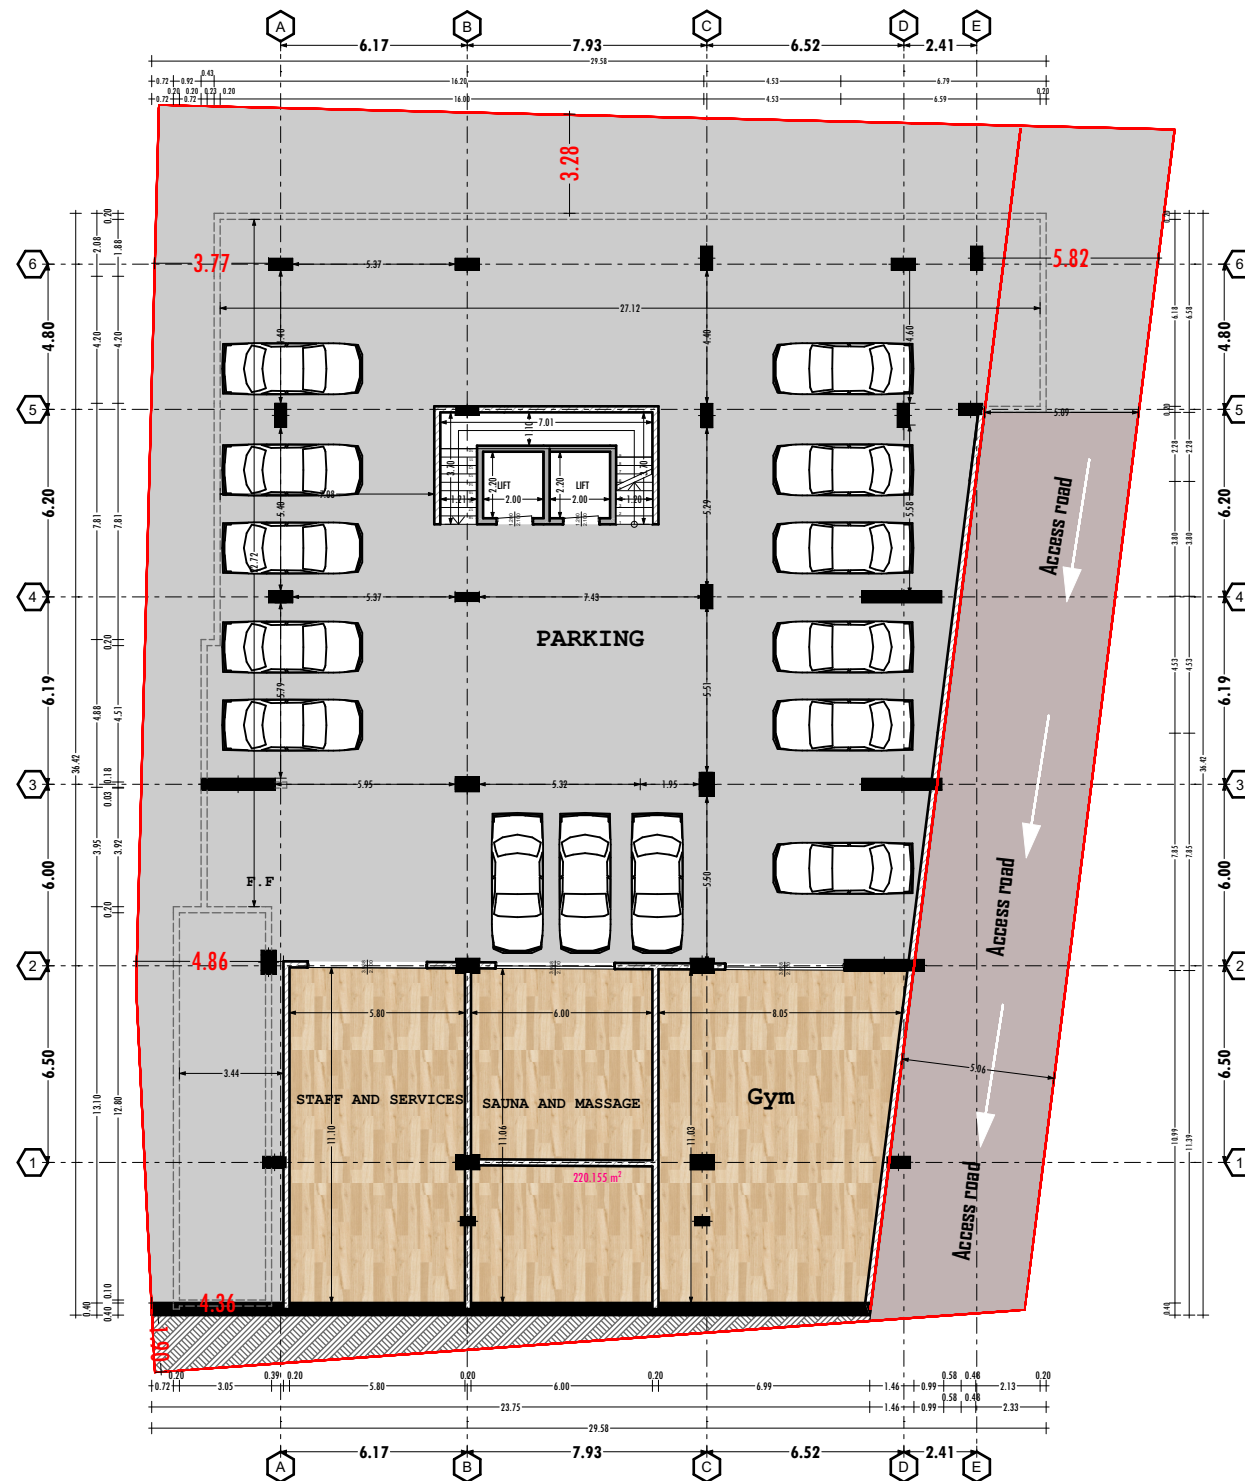

BASEMENT FLOOR PLAN LAYOUT

REPUBLIC OF RWANDA
KIGALI CITY
GASABO DISTRICT
KIMIHURURA SECTOR
KIMIHURURA CELL
AMAJYAMBERE VILLAGE

NOTES
All dimensions to be checked on site for all discrepancies and confirm with the architect.
DPC course to be provided under all walls.
Drainage under driveways and slabs to be encased in 150mm thick concrete surround.
All plumbing and drainage works to comply with M.O.H regulations.
All basins, baths, and sinks to be fitted with anti vacuum traps.
All softwood to be cured and approved to be polished and painted.
All S.W.V.P to be approved 100mm dia p.v.c. pipe encased with chicken mesh and concrete surround to be plastered and painted or finished in ceramic tiles.
Plinth level to be a minimum 500mm from proposed parking level or existing ground level.

RAINWATER
All pitched roofs to have 100*150mm 22 gauges box gutter and 75mm dia p.v.c down pipes in duct and other appropriate accessories all to be painted.
Mortar for bonding to be strictly 1:4 mixing ratio.

COPYRIGHT
This drawing is protected under the copyright act, and cannot be used or reproduced in part or in whole without the architect's approval.

LEAD CONSULTANTS
RAFIKI CONSTRUCTION COMPANY
B.P 5690, Tel: +250 - 788839442, Cell: +250 - 782566222
KIGALI - RWANDA

Owner:
NATAN PRIME LTD
PLOT N0: 1/02/08/02/1094 Kimihurura

DATE
Wednesday, 23 September 2026


Drawn by:
RCC Ltd

Checked by:
RCC Ltd

Zone: C1
Area: 1,276sqm

SCALE:
1:250

DOCUMENTS
BASEMENT FLOOR PLAN LAYOUT

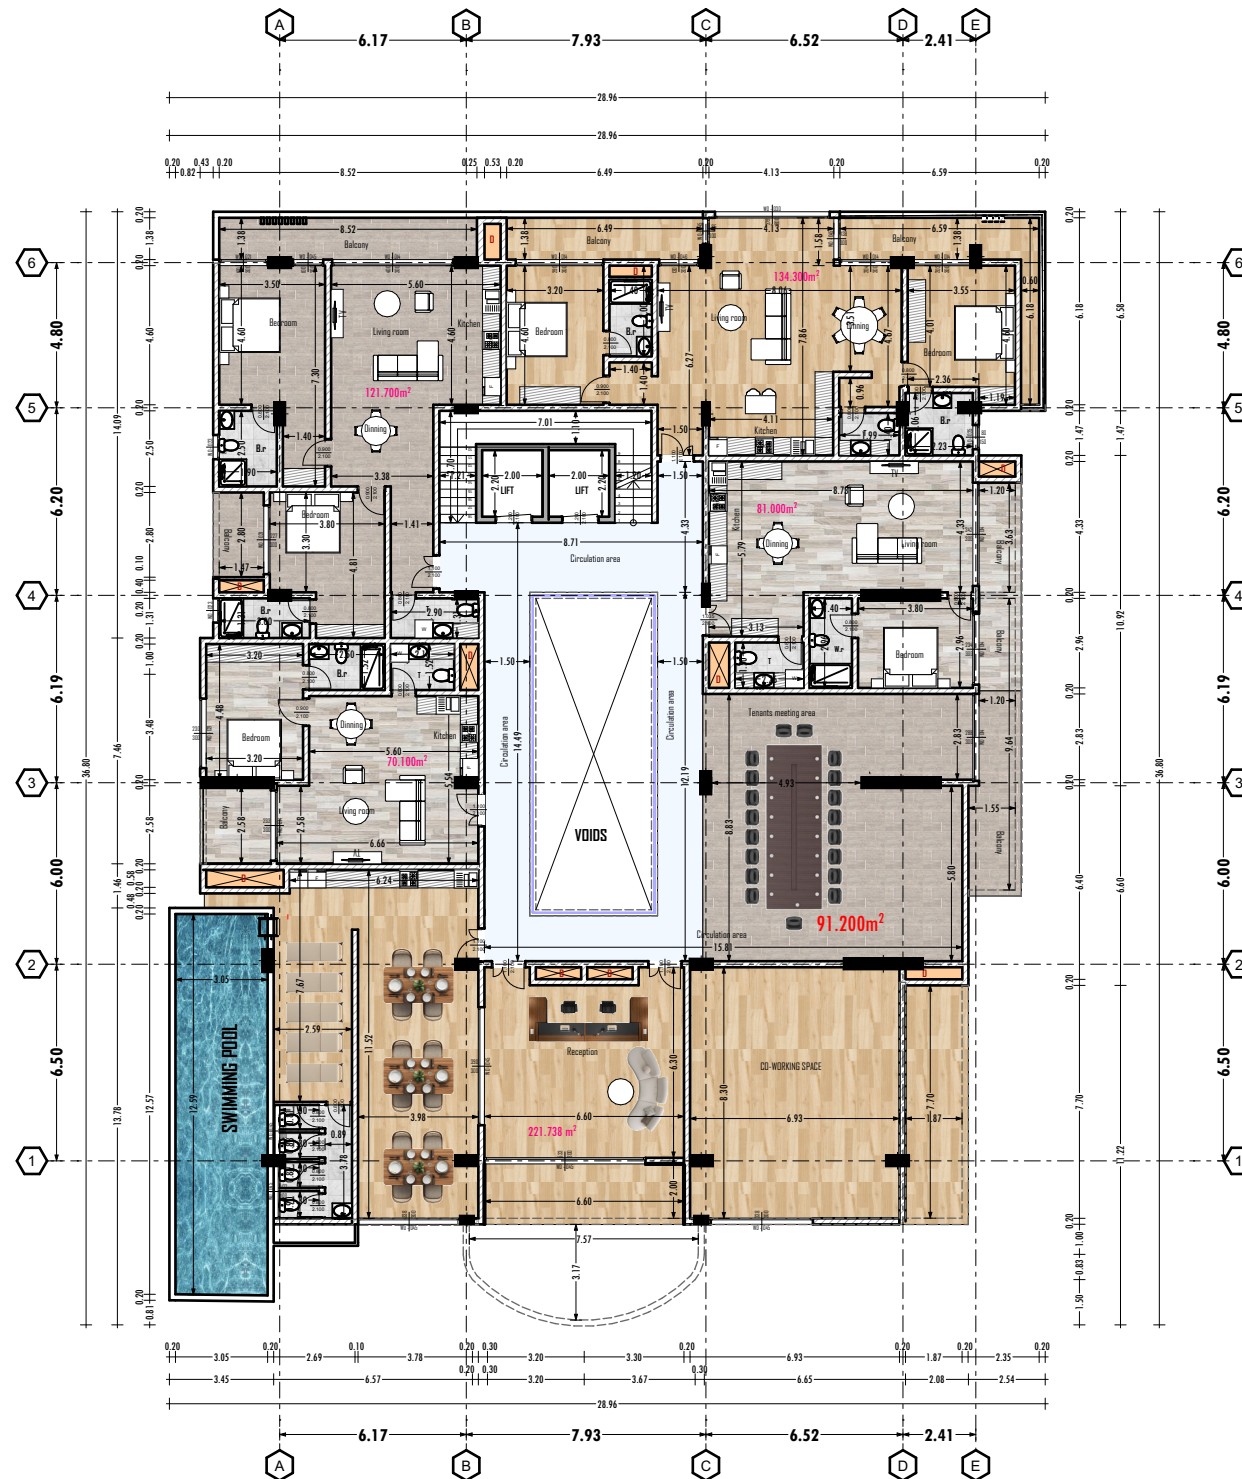

GROUND FLOOR PLAN LAYOUT

REPUBLIC OF RWANDA
KIGALI CITY
GASABO DISTRICT
KIMIHURURA SECTOR
KIMIHURURA CELL
AMAJYAMBERE VILLAGE

NOTES
All dimensions to be checked on site for all discrepancies and confirm with the architect.
DPC course to be provided under all walls.
Drainage under driveways and slabs to be encased in 150mm thick concrete surround.
All plumbing and drainage works to comply with M.O.H regulations.
All basins, bath, and sink to be fitted with anti vacuum taps.
All softwood to be cured and approved to be polished and painted.
All S&W.V.P to be approved 100mm dia p.v.c. pipe encased with chicken mesh and concrete surround to be plastered and painted or finished in ceramic tiles.
Plinth level to be a minimum 500mm from proposed parking level or existing ground level.

RAINWATER
All pitched roofs to have 100*150mm 22 gauges, box gutter and 75mm dia p.v.c down pipes in duct and other appropriate accessories all to be painted.
Mortar for bonding to be strictly 1:4 mixing ratio

COPYRIGHT
This drawing is protected under the copyright act, and cannot be used or reproduced in part or in whole without the architect's approval

LEAD CONSULTANTS



B.P 5690, Tel: +250-788329442, Cell: +250-782566222
KIGALI - RWANDA

Owner:

NATAN PRIME LTD

PLOT N0: 1/02/08/02/1094 Kimihurura

DATE
Wednesday, 23 September 2026

Drawn by:
RCC Ltd


Checked by:
RCC Ltd

Zone: C1
Area: 1,276sqm

SCALE:
1:250

DOCUMENTS

GROUND FLOOR
PLAN LAYOUT

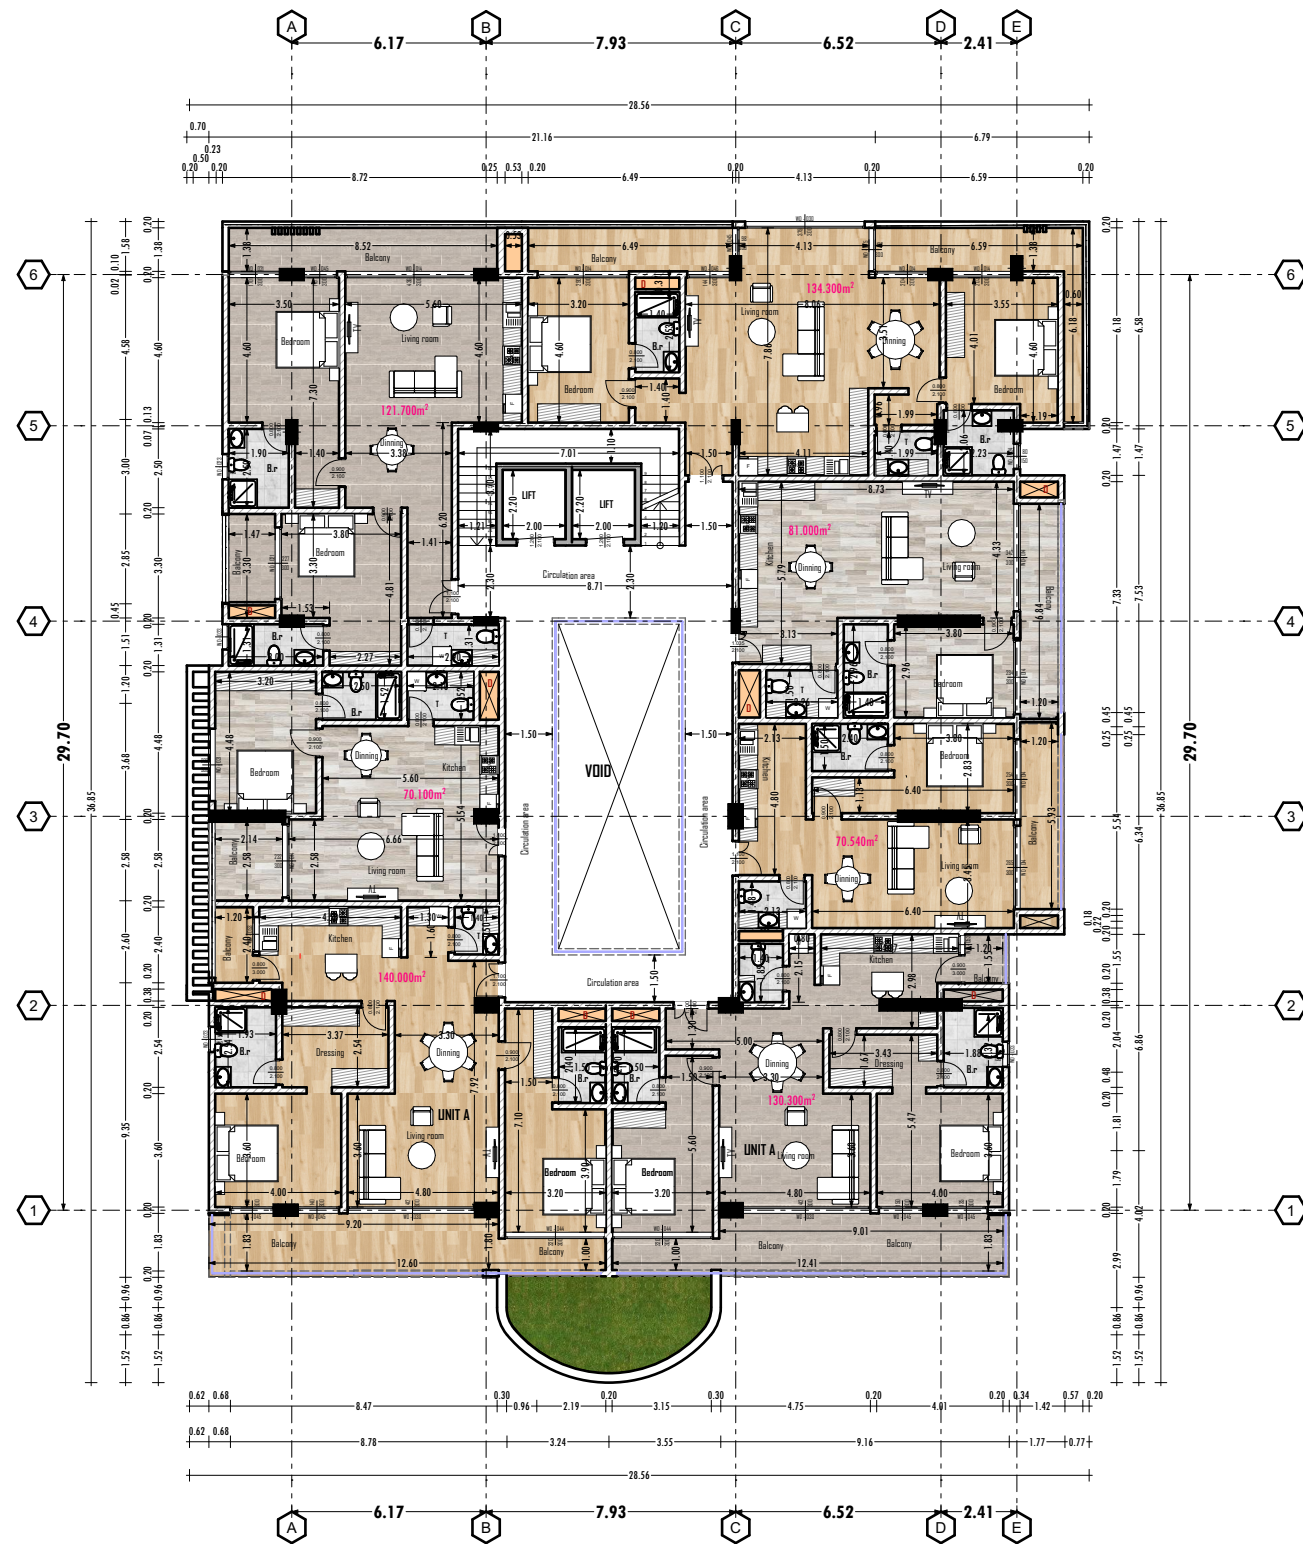

FIRST FLOOR PLAN

REPUBLIC OF RWANDA
KIGALI CITY
GASABO DISTRICT
KIMIHURURA SECTOR
KIMIHURURA CELL
AMAJYAMBERE VILLAGE

NOTES
All dimensions to be checked on site for all discrepancies and confirm with the architect.
DPC course to be provided under all walls.
Drainage under driveways and slabs to be encased in 150mm thick concrete surround.
All plumbing and drainage works to comply with M.O.H regulations.
All basins, baths, and sinks to be fitted with anti vacuum traps.
All softwood to be cured and approved to be polished and painted.
All S.W.V.P to be approved 100mm dia p.v.c. pipe encased with chicken mesh and concrete surround to be plastered and painted or finished in ceramic tiles.
Plinth level to be a minimum 500mm from proposed parking level or existing ground level.


RAINWATER
all pitched roofs to have 100*150mm 22 gauges box gutter and 75mm dia p.v.c down pipes in duct and other appropriate accessories all to be painted.
mortar for bonding to be strictly 1:4 mixing ratio

COPYRIGHT
This drawing is protected under the copyright act, and cannot be used or reproduced in part or in whole without the architect's approval

LEAD CONSULTANTS
RAFIKI
CONSTRUCTION COMPANY
R.P 5630, Tel: +250-78828462, Cell: +250-782566222
KIGALI - RWANDA

Owner:
NATAN PRIME LTD
PLOT N0: 1/02/08/02/1094 Kimihurura

DATE Wednesday, 23 September 2026		DOCUMENTS FIRST FLOOR PLAN LAYOUT
Drawn by: RCC Ltd	Checked by: RCC Ltd	
Zone: C1	SCALE: 1:240	
Area: 1,276sqm		

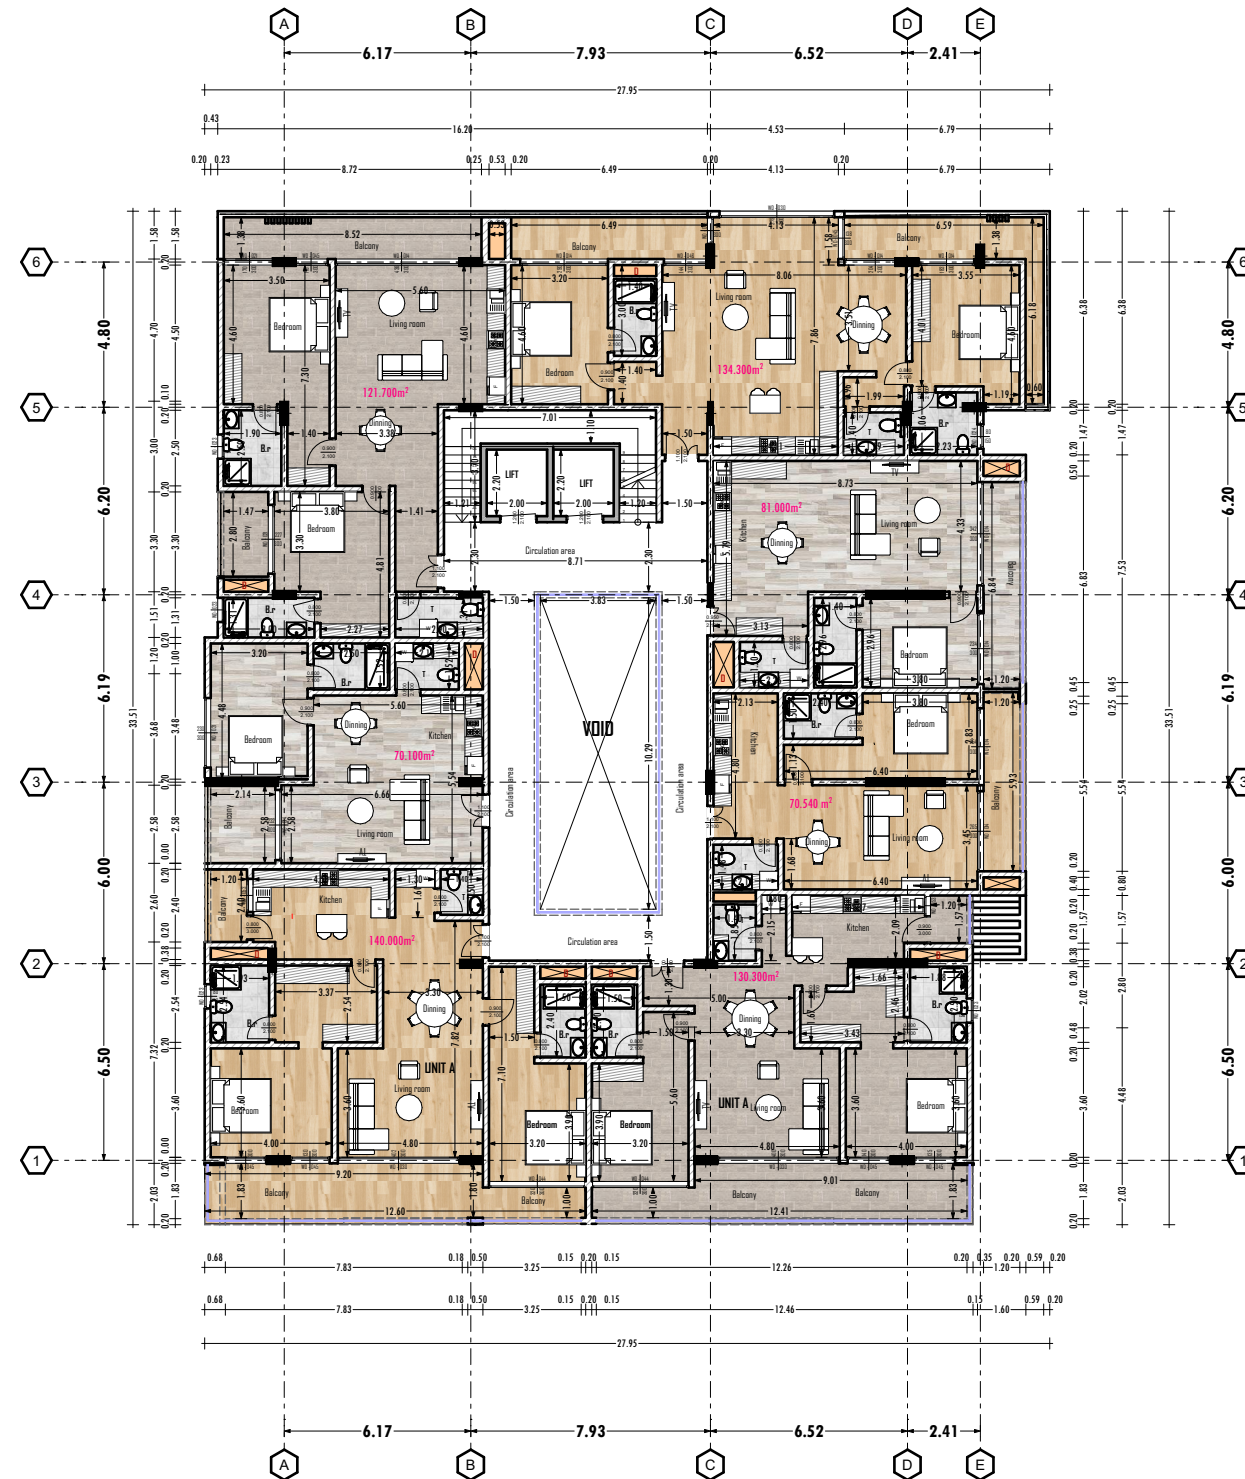

TYPICAL SECOND TO THIRD FLOOR PLAN

REPUBLIC OF RWANDA
KIGALI CITY
GASABO DISTRICT
KIMIHURURA SECTOR
KIMIHURURA CELL
AMAJYAMBERE VILLAGE

NOTES
All dimensions to be checked on site for all discrepancies and confirm with the architect.
DPC course to be provided under all walls.
Drainage under driveways and slabs to be encased in 150mm thick concrete surround.
All plumbing and drainage works to comply with M.O.H regulations.
All basins, baths, and sinks to be fitted with anti vacuum traps.
All softwood to be cured and approved to be polished and painted.
All S.W.V.P to be approved 100mm dia p.v.c. pipe encased with chicken mesh and concrete surround to be plastered and painted or finished in ceramic tiles.
Plinth level to be a minimum 500mm from proposed parking level or existing ground level.

RAINWATER
all pitched roofs to have 100*150mm 22 gauges box gutter and 75mm dia p.v.c down pipes in duct and other appropriate accessories all to be painted.
mortar for bonding to be strictly 1:4 mixing ratio

COPYRIGHT
This drawing is protected under the copyright act, and cannot be used or reproduced in part or in whole without the architect's approval

LEAD CONSULTANTS



B.P 5690, Tel: +250-788328442, Cell: +250-782566222
KIGALI - RWANDA

Owner:

NATAN PRIME LTD

PLOT N0: 1/02/08/02/1094 Kimihurura

DATE
Wednesday, 23 September 2026

Drawn by:
RCC Ltd


Checked by:
RCC Ltd

Zone: C1
Area: 1,276sqm

SCALE:
1:250

DOCUMENTS

TYPICAL SECOND
TO THIRD FLOOR
PLAN LAYOUT

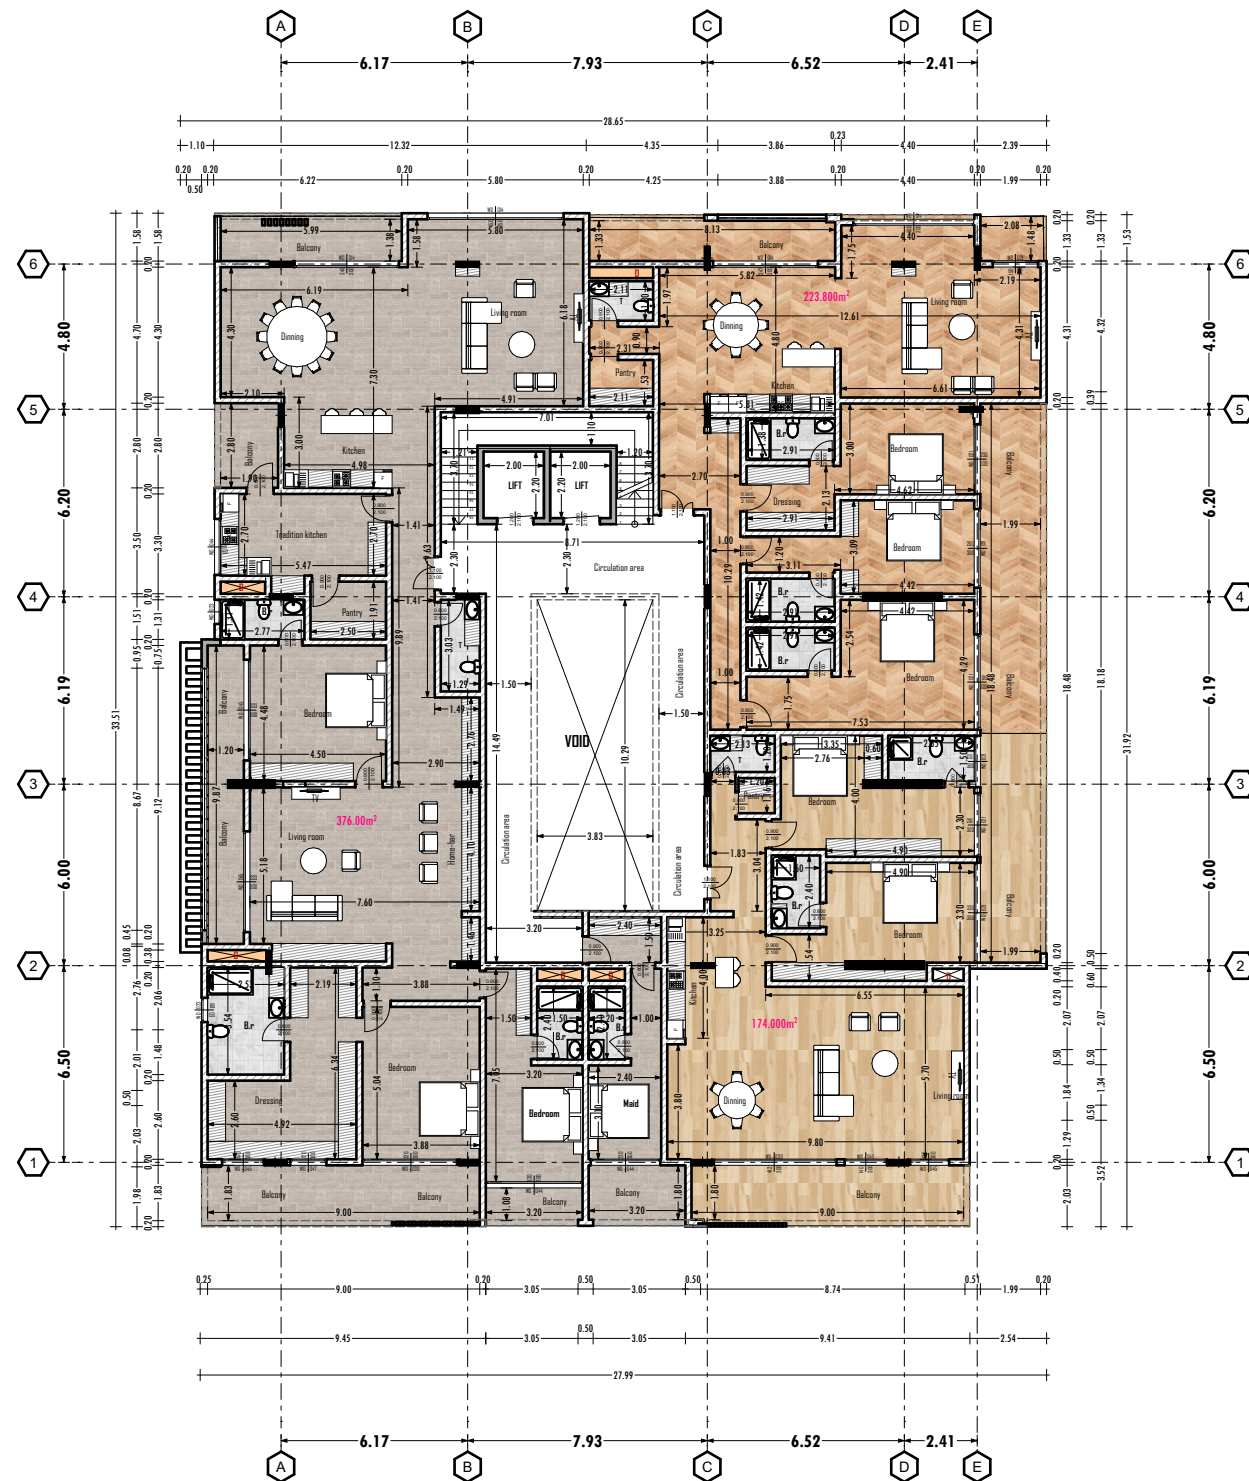

FOURTH FLOOR PLAN LAYOUT

REPUBLIC OF RWANDA
KIGALI CITY
GASABO DISTRICT
KIMIHURURA SECTOR
KIMIHURURA CELL
AMAJYAMBERE VILLAGE

NOTES
All dimensions to be checked on site for all discrepancies and confirm with the architect.
D.P.C. course to be provided under all walls.
Drainage under driveways and slabs to be encased in 150mm thick concrete surround.
All plumbing and drainage works to comply with M.O.H regulations.
All basins, baths, and sink to be fitted with anti vacuum taps.
All softwood to be cured and approved to be polished and painted.
All S.W.V.P to be approved 100mm dia p.v.c. pipe encased with chicken mesh and concrete surround to be plastered and painted or finished in ceramic tiles.
Plinth level to be a minimum 500mm from proposed parking level or existing ground level.

RAINWATER
all pitched roofs to have 100*150mm 22 gauges box gutter and 75mm dia p.v.c down pipes in duct and other appropriate accessories all to be painted.
mortar for bonding to be strictly 1:4 mixing ratio

COPYRIGHT
This drawing is protected under the copyright act, and cannot be used or reproduced in part or in whole without the architect's approval

LEAD CONSULTANTS



B.P 5630, Tel: +250 - 788328442, Cell: +250 - 782566222
KIGALI - RWANDA

Owner:

NATAN PRIME LTD

PLOT N0: 1/02/08/02/1094 Kimihurura

DATE

Wednesday, 23 September 2026

Drawn by:

RCC Ltd

Checked by:

RCC Ltd

Zone: C1


Area: 1,276sqm

SCALE:

1:250

DOCUMENTS

FOURTH FLOOR
PLAN LAYOUT

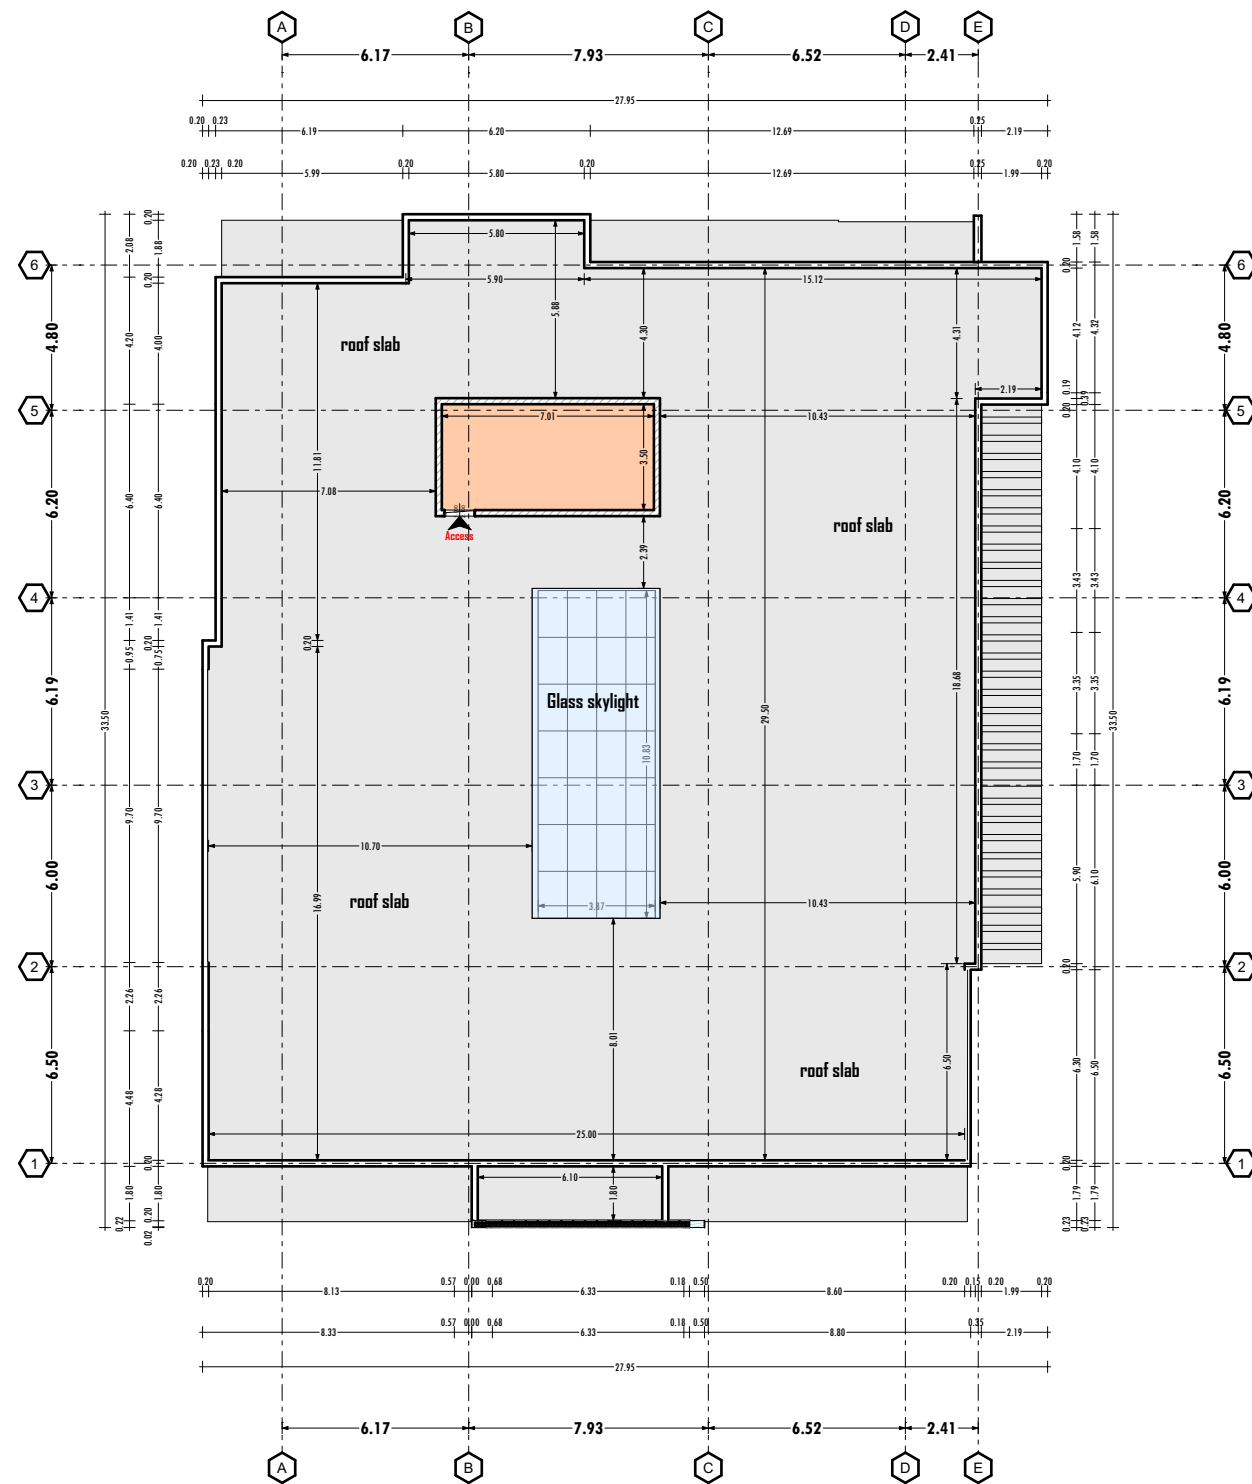

ROOF PLAN LAYOUT

REPUBLIC OF RWANDA
KIGALI CITY
GASABO DISTRICT
KIMIHURURA SECTOR
KIMIHURURA CELL
AMAJYAMBERE VILLAGE

NOTES
All dimensions to be checked on site for all discrepancies and confirm with the architect.
DPC course to be provided under all walls.
Drainage under driveways and slabs to be encased in 150mm thick concrete surround.
All plumbing and drainage works to comply with M.O.H regulations.
All basins, bath, and sink to be fitted with anti vacuum taps.
All softwood to be cured and approved to be polished and painted.
All S.W.V.P to be approved 100mm dia p.v.c. pipe encased with chicken mesh and concrete surround to be plastered and painted or finished in ceramic tiles.
Plinth level to be a minimum 500mm from proposed parking level or existing ground level.

RAINWATER
all pitched roofs to have 100*150mm 22 gauges box gutter and 75mm dia p.v.c down pipes in duct and other appropriate accessories all to be painted.
mortar for bonding to be strictly 1:4 mixing ratio

COPYRIGHT
This drawing is protected under the copyright act, and cannot be used or reproduced in part or in whole without the architect's approval

LEAD CONSULTANTS
RAFIKI
CONSTRUCTION COMPANY
B.P 5690, Tel: +250 - 788284442, Cell: +250 - 782566222
KIGALI - RWANDA

Owner:
NATAN PRIME LTD
PLOT N0: 1/02/08/02/1094 Kimihurura

DATE
Wednesday, 23 September 2026
Drawn by:
RCC Ltd
Checked by:
RCC Ltd
Zone: C1
Area: 1,276sqm
SCALE:
1:250

DOCUMENTS
ROOF PLAN
LAYOUT